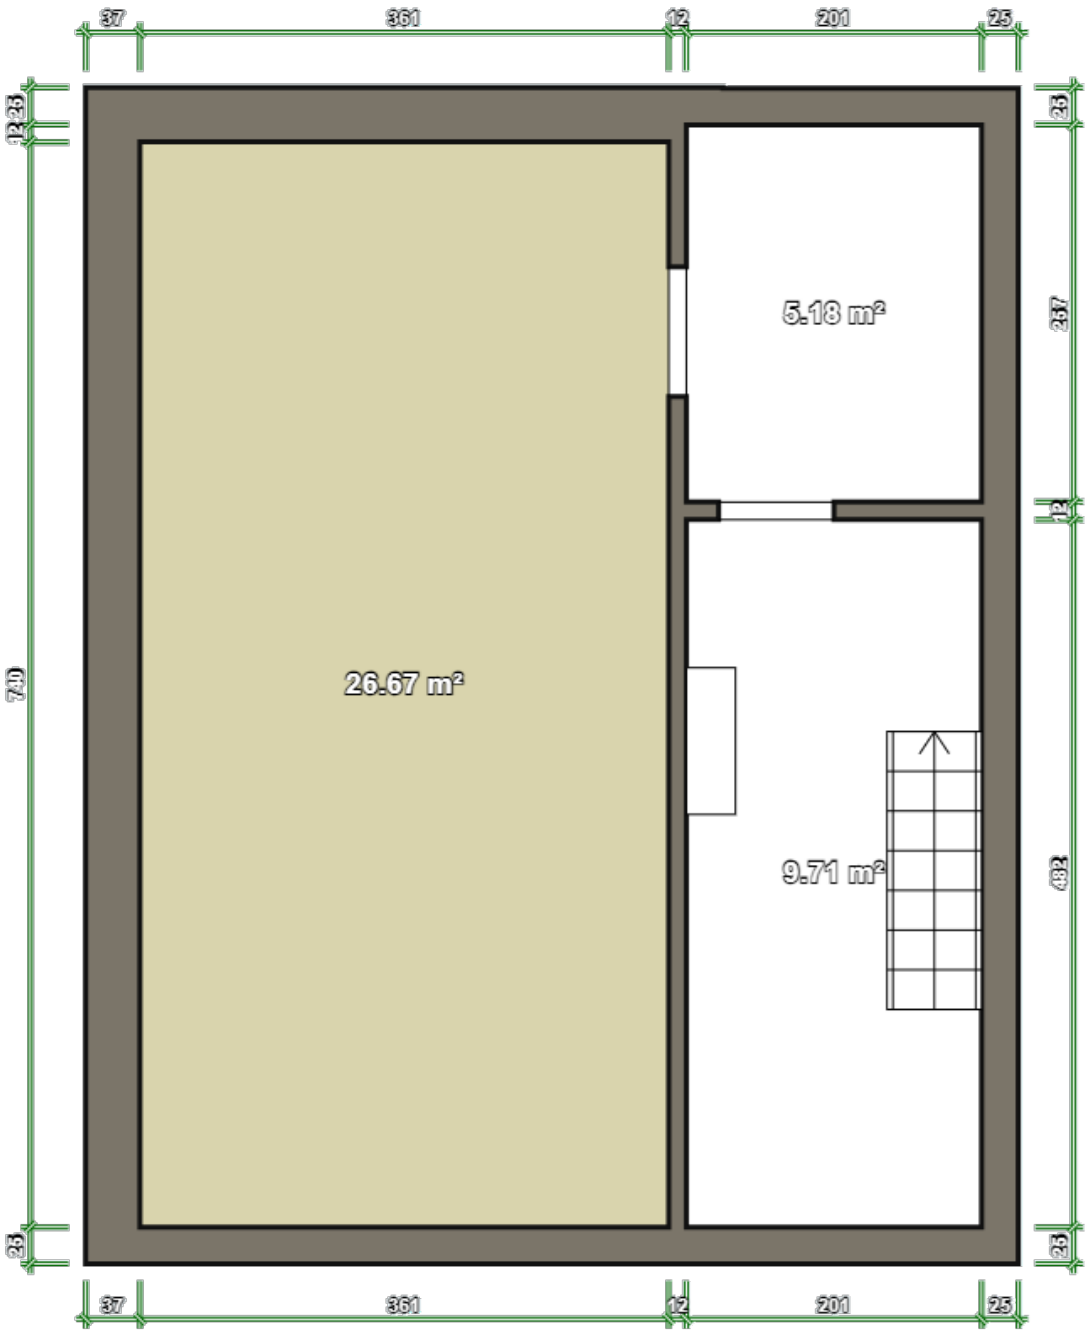
Kelder


37
361
12
201
25
23
12
23
5.18 m²
237
12
26.67 m²
9.71 m²
492
23
23
37
361
12
201
25

Gelijkvloers

Linksboven is de veranda, midden boven is de keuken, onder de trap is een wc


Op deze verdieping moet komen:

De keuken met elektrische kookplaat, oven, afwasmachine, ijskast

Een bureau

Een plaats voor was- en droogkast


Een eettafel en een zetel+tv

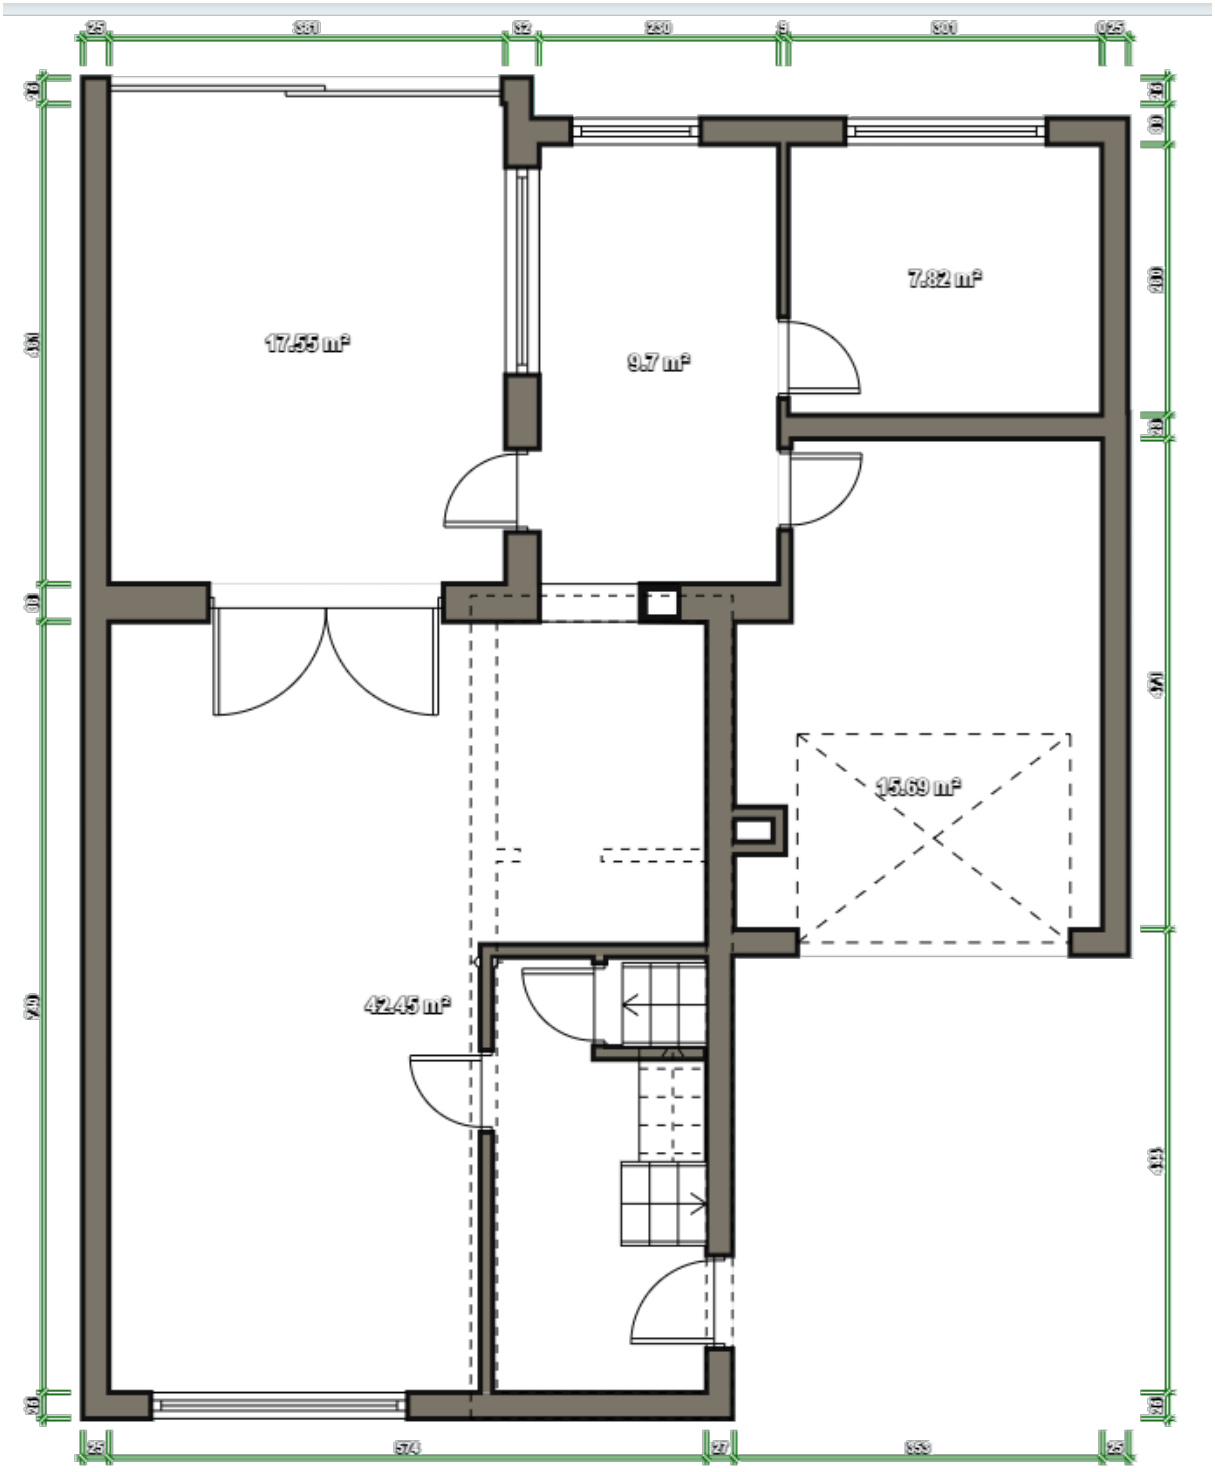

1e verdieping

Op deze verdieping is een badkamer, 2 slaapkamers en een bureau

De badkamer heeft een bad, een wc, een wastafel met elektrische spiegel en een elektrische verwarming

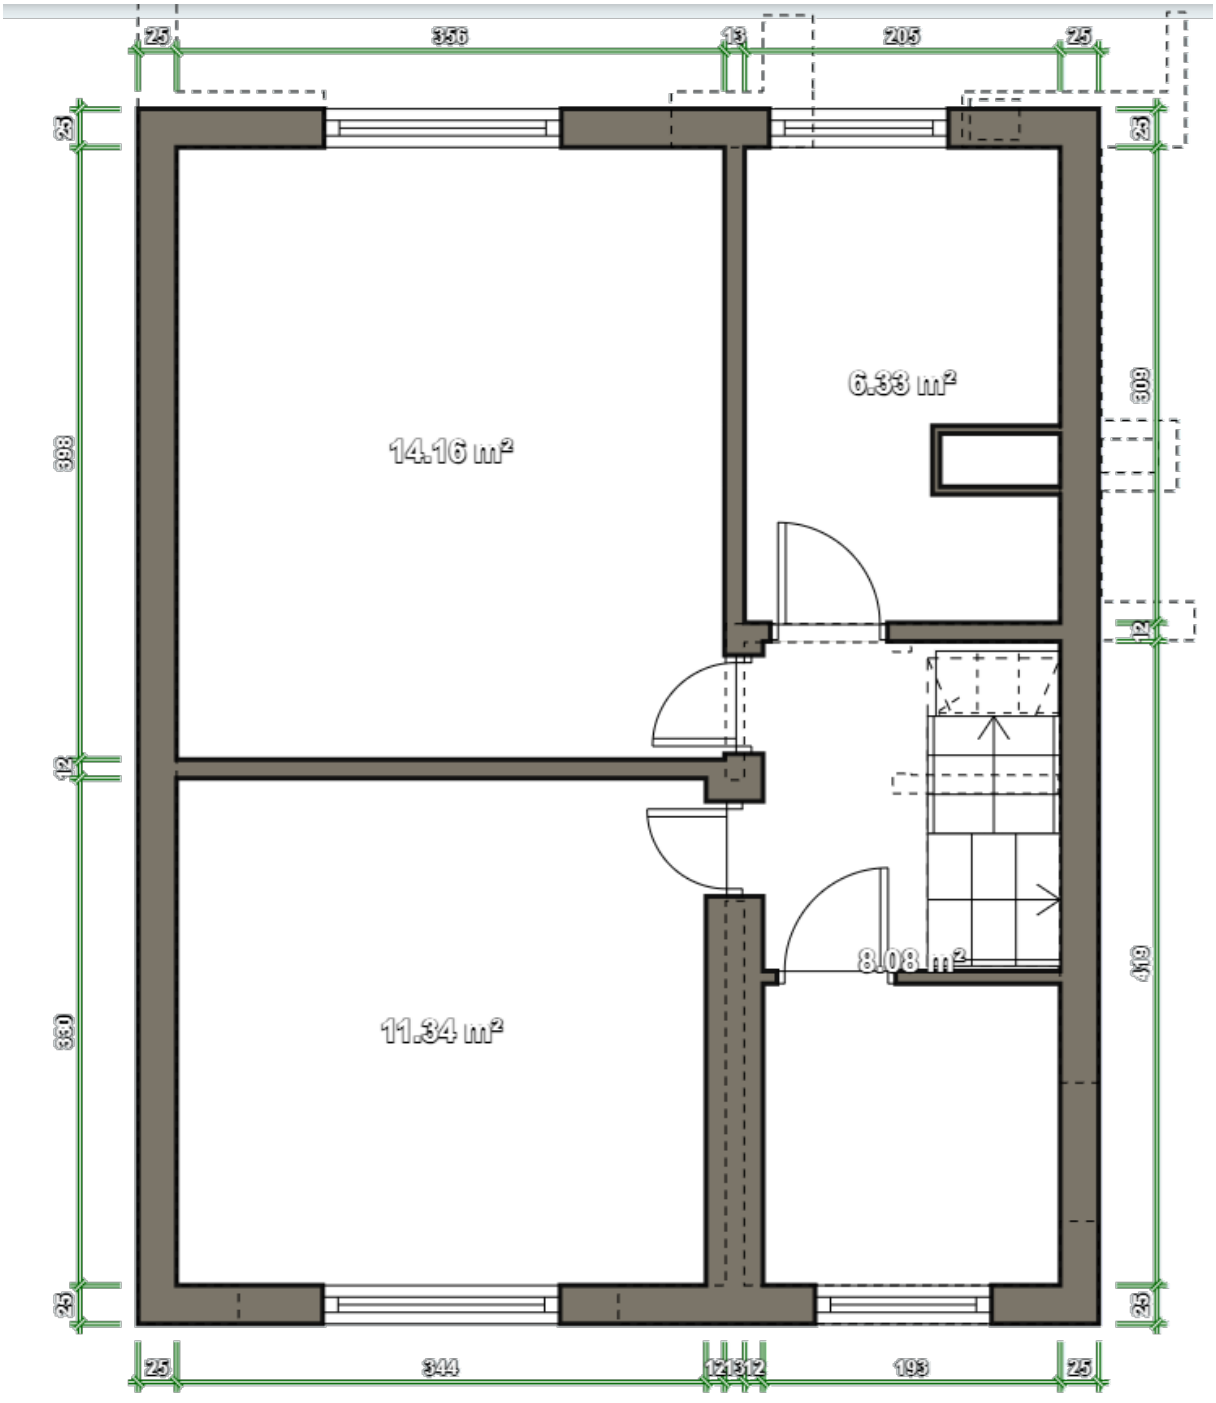

Zolder

Deze verdieping heeft 2 slaapkamers met elk een klein bureau.

